

杭州市不动产登记信息查询记录

编号: 2025-bdcadminwangsm-009151

依 杭州市余杭区人民法院 申请查询坐落于 杭州市余杭区仁和街道清合嘉园东区7幢2单元302室 的
不动产登记信息, 经查询杭州市不动产登记信息管理系统, 结果如下:

不动产坐落		杭州市余杭区仁和街道清合嘉园东区7幢2单元302室					
用途	城镇住宅用地/住宅	建筑面积(m²)	124.27	土地使用权面积(m²)	71.9	使用期限	2005年03月08日至2075年03月07日
限制信息		不动产:有查封,有抵押				宗地号	330110109001GB03043
不动产状况	权利人						
	权证号(证明号)	浙(2021)余杭区不动产权第0012511号					
	权利类型	国有建设用地使用权/房屋(构筑物)所有权		权利性质		出让/存量房产	
	共有情况	共同共有		登记日期		2021年01月26日	
	权利状态	现状					
	附记	换证,原权证号杭余商国用(2012)第08214号/余房权证仁更字第12119376号、余房权证仁更字第12134501号。1、不动产权利为共同共有;2、本宗地内未作分摊的土地使用权属全体业主共用。					
抵押状况	抵押权人			登记证明号		浙(2021)余杭区不动产证明第0013274号	
	抵押方式	最高额抵押		债权数额		300万元	
	登记日期	2021年01月28日		债务履行期限(债权确定期间)		2021年01月26日起2027年01月25日止	
	附记	债务人:杭州龙科蔬菜有限公司					
查封状况	查封文号	(2023)津0116执保5735号					
	查封期限	2023年11月15日起2026年11月14日止					
	查封机关	天津市滨海新区人民法院					
查封状况	查封文号	(2023)沪0117民初21397号					
	查封期限	2023年11月17日起2026年11月16日止					
	查封机关	上海市松江区人民法院					
查封状况	查封文号	(2023)沪0112民初53482号					
	查封期限	2023年12月28日起2026年12月27日止					
	查封机关	上海市闵行区人民法院					
查封状况	查封文号	(2024)浙0110执保41号					
	查封期限	2024年01月23日起2027年01月22日止					
	查封机关	杭州市余杭区人民法院					

查封状况	查封文号	(2024)浙0110执2574号
	查封期限	2024年07月05日起2027年07月04日止
	查封机关	杭州市余杭区人民法院
查封状况	查封文号	(2024)浙0102执6452号
	查封期限	2024年12月04日起2027年12月03日止
	查封机关	杭州市上城区人民法院
查封状况	查封文号	(2024)浙0110执4797号
	查封期限	2024年12月12日起2027年12月11日止
	查封机关	杭州市余杭区人民法院
查封状况	查封文号	(2024)浙0102执5542号
	查封期限	2024年12月12日起2027年12月11日止
	查封机关	杭州市上城区人民法院
查封状况	查封文号	(2025)浙0110执896号
	查封期限	2025年03月12日起2028年03月11日止
	查封机关	杭州市余杭区人民法院
查封状况	查封文号	(2024)浙0782执保10760号
	查封期限	2025年03月20日起2028年03月19日止
	查封机关	义乌市人民法院
查封状况	查封文号	(2025)浙0110执2158号
	查封期限	2025年03月26日起2028年03月25日止
	查封机关	杭州市余杭区人民法院
查封状况	查封文号	(2025)浙0110执2495号
	查封期限	2025年03月26日起2028年03月25日止
	查封机关	杭州市余杭区人民法院
查封状况	查封文号	(2025)浙0110执4417号
	查封期限	2025年06月20日起2028年06月19日止
	查封机关	杭州市余杭区人民法院
居住权状况	无	
地役权状况	无	
异议状况	无	

该记录依申请用于 法院委托评估。

说明:


- 1、本查询记录范围为办理过登记的不动产登记信息(不含预售合同备案信息)，涵盖杭州市上城区、拱墅区、西湖区、钱塘区、滨江区、萧山区、余杭区、临平区、富阳区、临安区和淳安县、桐庐县、建德市。
- 2、本查询记录涉及到萧山区、余杭区、临平区、富阳区、临安区、淳安县、桐庐县、建德市属地不动产查封的，请至属地进一步核实不动产信息。
- 3、申请人请当场核实以上身份信息和结果信息，如信息有误请及时告知工作人员，如隐瞒不报或提供虚假信息的需自行承担法律责任。
- 4、申请人对以上查询中涉及国家秘密、个人隐私和商业秘密的信息负有保密义务，不得泄露给他人，也不得不正当使用。

房产分层分户平面图

图幅号:

房屋座落	杭州市余杭区仁和镇清合嘉园东区7幢2单元302室			地号	
建成年份	2008	所在层次	3	套内面积(㎡)	111.24
设计用途	住宅	地上总层数	6	分摊面积(㎡)	13.03
建筑结构	钢筋混凝土	地下总层数		建筑面积(㎡)	124.27

53062008

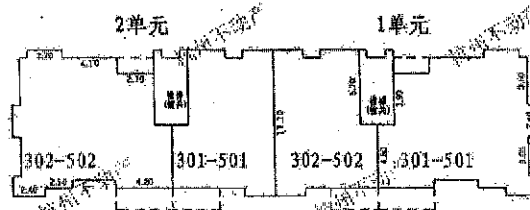

三至五层中轴图

比例尺

1:500


杭州不动产

036

杭州清东房地产开发有限公司(清东嘉园东区)宗地图

73-101 6 A

地籍调查表
登记簿

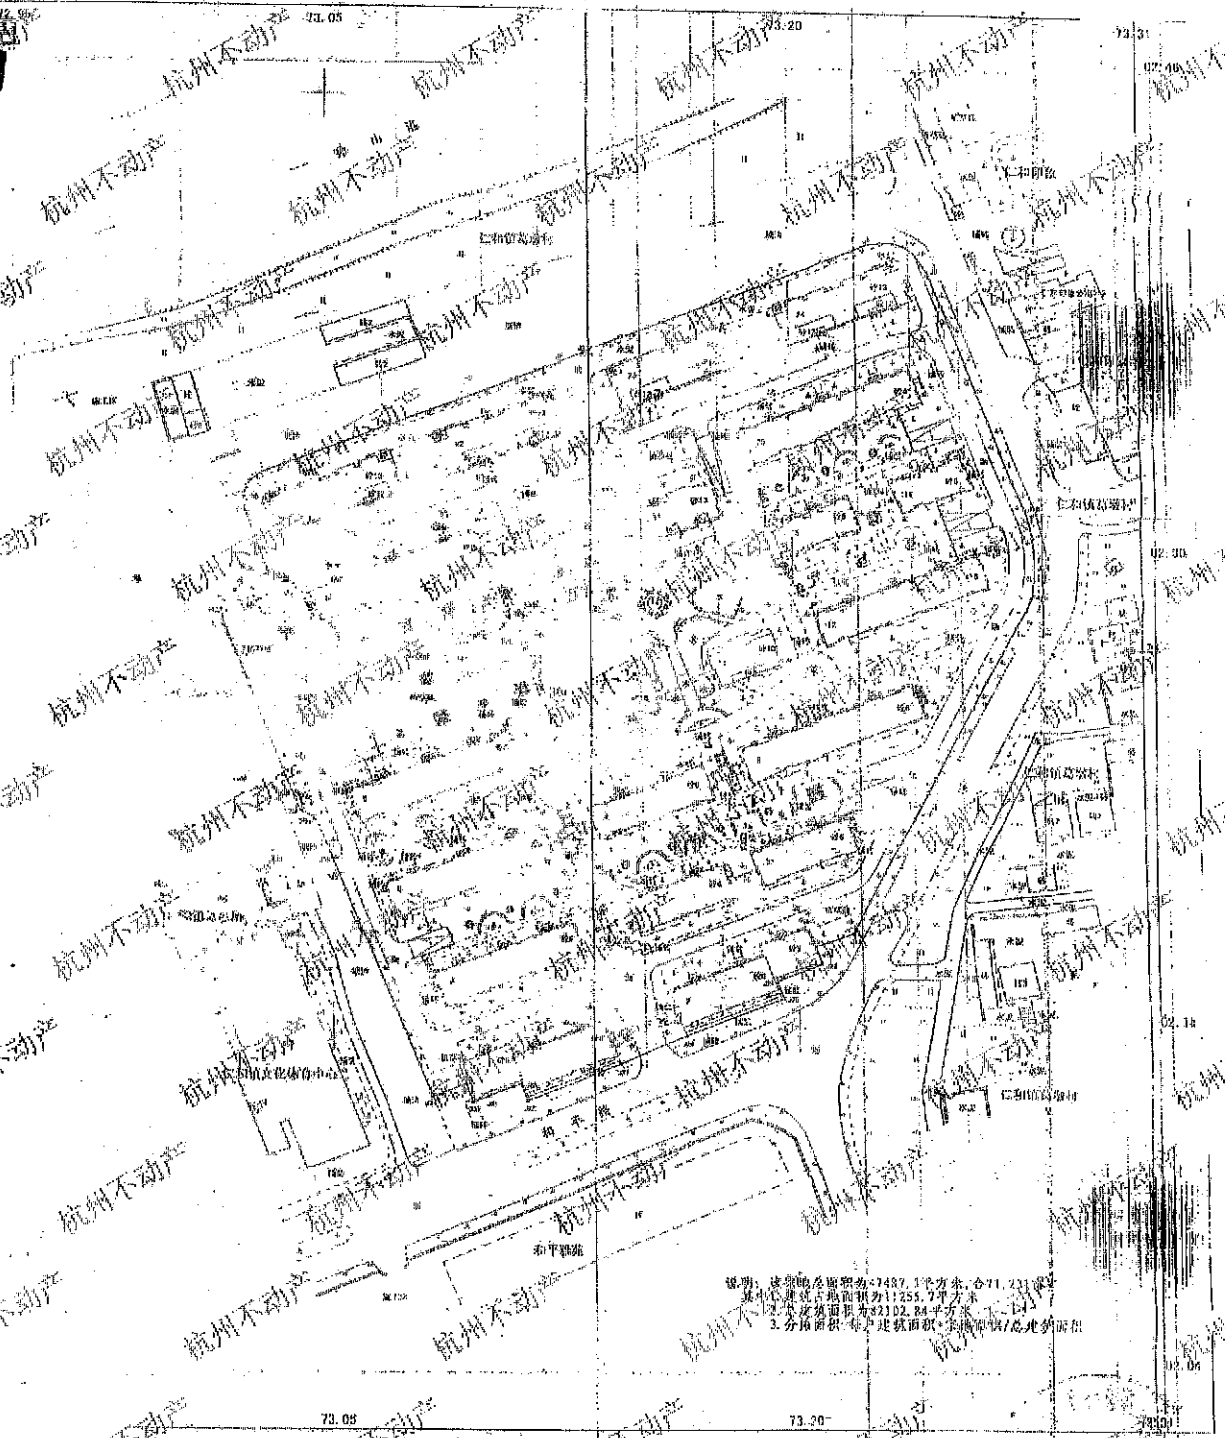

说明: 该宗地总用地面积为7487.1平方米, 合71.233公顷
其中: 建设用地面积为11255.7平方米
总建筑面积为32102.84平方米
3. 分宗面积: 各宗地面积、宗地面积、宗地面积

宗地面积: 7487.1平方米
宗地面积: 11255.7平方米
宗地面积: 32102.84平方米

