

杭州市不动产登记信息查询记录

编号：2025-bdcadminwangsm-001704

依 杭州市余杭区人民法院 申请查询坐落于 杭州市余杭区仁和街道尚堂久里10幢1单元502室 的不动
产登记信息，经查询杭州市不动产登记信息管理系统，结果如下：

不动产坐落		杭州市余杭区仁和街道尚堂久里10幢1单元502室					
用途	住宅	建筑面积 (m²)	89.35	土地使用权 面积 (m²)		使用期限	—
限制信息	不动产:无查封,无抵押,有预告查封,有预告抵押					宗地号	330110109005GB00949
不动产状况	权利人						
	权证号 (证明号)	浙(2020)余杭区不动产证明第0056298号					
	权利类型	国有建设用地使用权	权利性质		出让		
	共有情况	—	登记日期		2020年06月05日		
	权利状态	预告登记					
	附记	—					
抵押状况	抵押权人	中国农业银行股份有限公司杭州之江支行		登记证明号		浙(2020)余杭区不动产证明第0056299号	
	抵押方式	一般抵押		债权数额		70万元	
	登记日期	2020年06月05日		债务履行期限 (债权确定期间)		2020年05月21日起2050年05月20日止	
	附记	—					
查封状况	查封文号	(2023)浙0110执保1473号					
	查封期限	2024年01月02日起2027年01月01日止					
	查封机关	杭州市余杭区人民法院					
查封状况	查封文号	(2023)浙0110执保1464号					
	查封期限	2024年01月02日起2027年01月01日止					
	查封机关	杭州市余杭区人民法院					
查封状况	查封文号	(2023)浙0110执保1511号					
	查封期限	2024年01月02日起2027年01月01日止					
	查封机关	杭州市余杭区人民法院					
查封状况	查封文号	(2023)浙0110执保1481号					
	查封期限	2024年01月03日起2027年01月02日止					
	查封机关	杭州市余杭区人民法院					
查封状况	查封文号	(2024)浙0110执4001-1号					
	查封期限	2024年11月07日起2027年11月06日止					
	查封机关	杭州市余杭区人民法院					

查封状况	查封文号	(2024)浙0110执4001-2号
	查封期限	2024年11月07日起2027年11月06日止
	查封机关	杭州市余杭区人民法院
居住权状况	无	
地役权状况	无	
异议状况	无	

该记录依申请用于 案件调查 。



说明：

- 1、本查询记录范围为办理过登记的不动产登记信息(不含预售合同备案信息)，涵盖杭州市上城区、拱墅区、西湖区、钱塘区、滨江区、萧山区、余杭区、临平区、富阳区、临安区和淳安县、桐庐县、建德市。
- 2、本查询记录涉及到萧山区、余杭区、临平区、富阳区、临安区、淳安县、桐庐县、建德市属地不动产查封的，请至属地进一步核实不动产信息。
- 3、申请人请当场核实以上身份信息 and 结果信息，如信息有误请及时告知工作人员，如隐瞒不报或提供虚假信息的，需自行承担法律责任。
- 4、申请人对以上查询中涉及国家秘密、个人隐私和商业秘密的信息负有保密义务，不得泄露给他人，也不得不正当使用。

杭州市不动产登记信息查询记录

编号: 2025-bdcadminwangsm-001703

依 杭州市余杭区人民法院 申请查询坐落于 杭州市余杭区仁和街道尚堂久里10幢1单元502室 的不动
产登记信息, 经查询杭州市不动产登记信息管理系统, 结果如下:

不动产坐落		杭州市余杭区仁和街道尚堂久里10幢1单元502室					
用途	城镇住宅用地 /住宅	建筑面积 (m²)	89.35	土地使用权 面积 (m²)	5.3	使用期限	2018年05月25日至 2088年05月24日
限制信息		不动产:无查封,无抵押,有预告查封,有预告,有预告抵押				宗地号	330110109005GB00949
不动产状况	权利人	杭州益光房地产开发有限公司					
	权证号 (证明号)	浙(2021)杭州市不动产权第2074551号					
	权利类型	国有建设用地使用权 /房屋(构筑物)所有 权		权利性质		出让/市场化商品房	
	共有情况	单独所有		登记日期		2021年11月18日	
	权利状态	现状					
	附记	1、商品房; 2、本宗地内未作分摊的土地使用权属全体业主共用。					
抵押状况	无						
查封状况	无						
居住权状况	无						
地役权状况	无						
异议状况	无						

该记录依申请用于 案件调查 。



说明:

- 1、本查询记录范围为办理过登记的不动产登记信息(不含预售合同备案信息), 涵盖杭州市上城区、拱墅区、西湖区、钱塘区、滨江区、萧山区、余杭区、临平区、富阳区、临安区和淳安县、桐庐县、建德市。
- 2、本查询记录涉及到萧山区、余杭区、临平区、富阳区、临安区、淳安县、桐庐县、建德市属地不动产查封的, 请至属地进一步核实不动产信息。
- 3、申请人请当场核实以上身份信息 and 结果信息, 如信息有误请及时告知工作人员, 如隐瞒不报或提供虚假信息的, 需自行承担法律责任。
- 4、申请人对以上查询中涉及国家秘密、个人隐私和商业秘密的信息负有保密义务, 不得泄露给他人, 也不得不正当使用。

房产分层分户平面图

2540

图幅号:

房屋座落	杭州市余杭区仁和街道尚堂久里10幢1单元502室			地号	
建成年份	2020	所在层次	5	套内面积(m ²)	69.30
设计用途	住宅	地上总层数	20	分摊面积(m ²)	20.05
建筑结构	钢筋混凝土	地下总层数	0	建筑面积(m ²)	89.35

53202020




二至二十层平面图

比例尺 1:500

宗地图

73-99.2-C、D 73-98.4-A、B

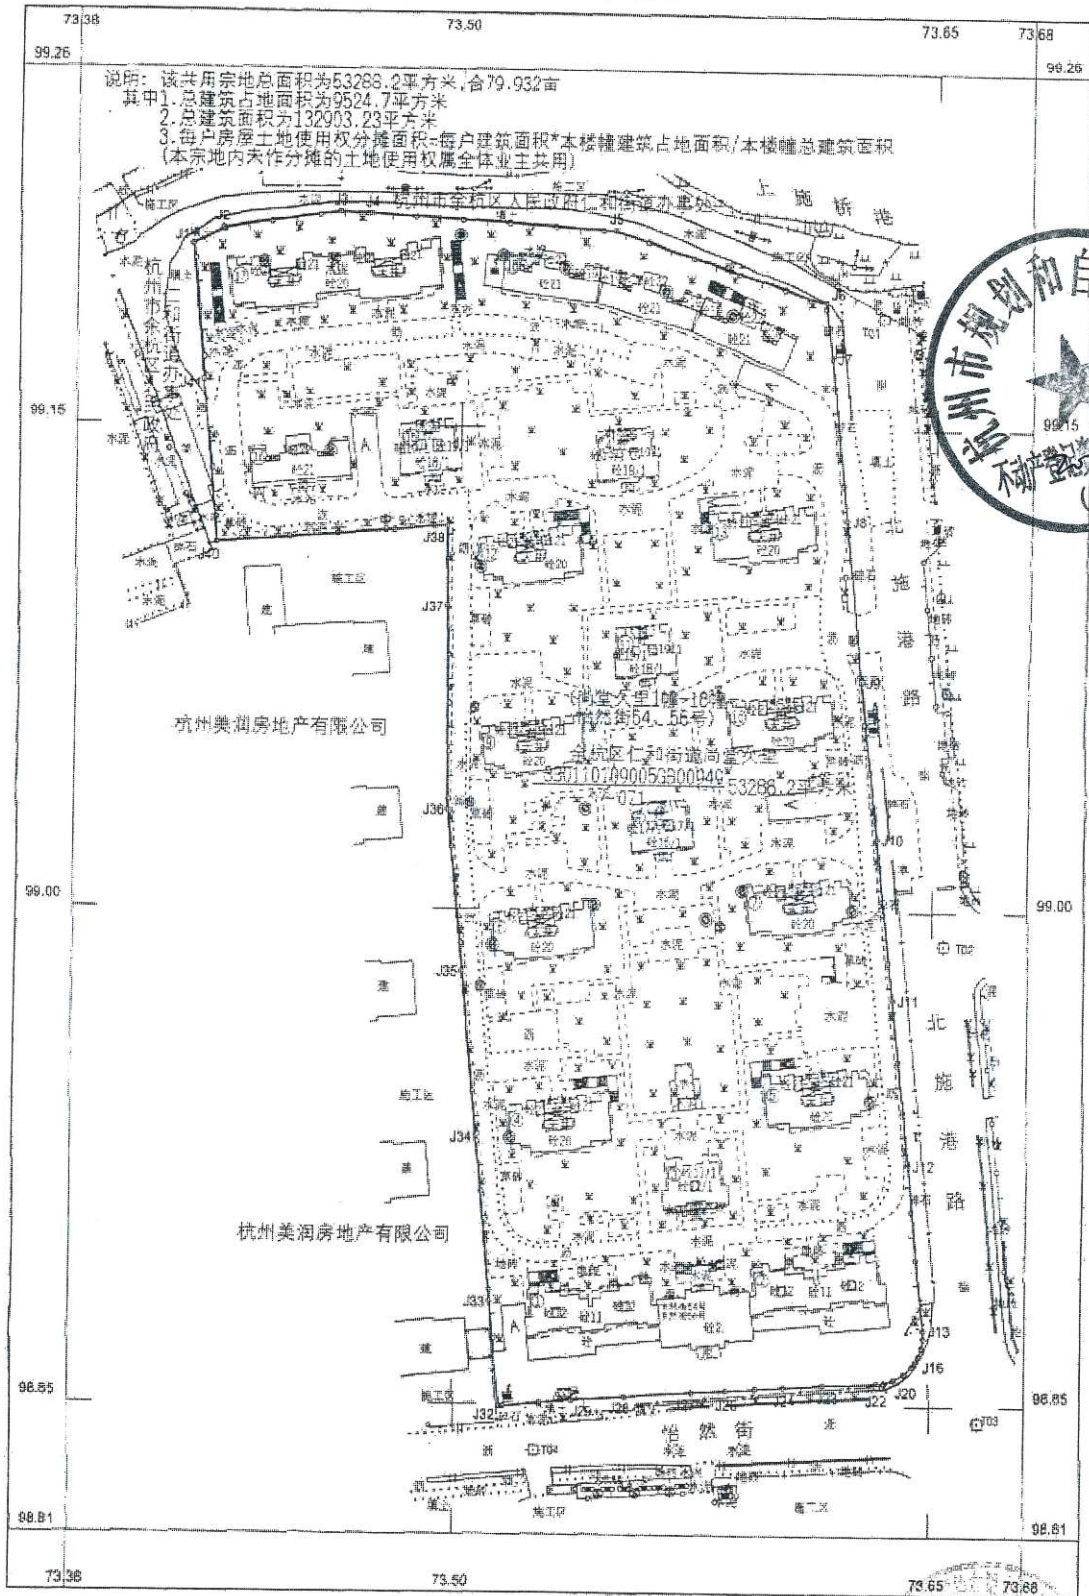

说明: 该共用宗地总面积为53288.2平方米,合79.932亩
 其中1.总建筑占地面积为9524.7平方米
 2.总建筑面积为132903.23平方米
 3.每户房屋土地使用权分摊面积=每户建筑面积*本楼幢建筑占地面积/本楼幢总建筑面积
 (本宗地内未作分摊的土地使用权属全体业主共用)

2021年1月Walk软件成图。
 杭州坐标系。
 2007年版图式。

1:1500

测量员: 何作时
 绘图员: 陈丹阳
 检查员: 毛小芳