

杭州市不动产登记信息查询记录

编号：2025-YHSMZJwangsm-021112

依 杭州市余杭区人民法院 申请查询坐落于 余杭区仁和街道仁和印象4幢2单元903室 的不动产登记信息，经查询杭州市不动产登记信息管理系统，结果如下：

不动产坐落		余杭区仁和街道仁和印象4幢2单元903室					
用途	住宅	建筑面积 (m²)	105.09	土地使用权 面积 (m²)	44.9	使用期限	2006年01月18日至 2076年01月17日
限制信息	房产:有查封,有抵押,土地:有查封,有抵押					宗地号	330110109001GB03046
不动产状况	权利人						
	权证号 (证明号)	余房权证仁移字第12033644号、余房权证仁移字第12135159号					
	权利类型	房屋(构筑物)所有权	权利性质		存量房产		
	共有情况	--	登记日期		2012年07月10日		
	权利状态	现状					
	附记	该房为 共同共有					
抵押状况	抵押权人		登记证明号		浙(2021)杭州市不动产证明第2086878号		
	抵押方式	最高额抵押	债权数额		217.8万元		
	登记日期	2021年12月23日	债务履行期限 (债权确定期间)		2021年12月14日起2031年12月14日止		
	附记	存在禁止或限制转让抵押不动产的约定债务人					
查封状况	查封文号	(2024)浙0281执902号					
	查封期限	2024年03月26日起2027年03月25日止					
	查封机关	余姚市人民法院					
查封状况	查封文号	(2024)浙0521民诉前调3926号					
	查封期限	2024年05月21日起2027年05月20日止					
	查封机关	浙江省德清县人民法院					
查封状况	查封文号	(2024)苏0904民初2986号					
	查封期限	2024年05月27日起2027年05月26日止					
	查封机关	江苏省盐城市大丰区人民法院					
查封状况	查封文号	(2024)苏0682执2549号					
	查封期限	2024年06月03日起2027年06月02日止					
	查封机关	江苏省如皋市人民法院					
查封状况	查封文号	(2024)浙0521执保1706号					
	查封期限	2024年06月24日起2027年06月23日止					
	查封机关	德清县人民法院					

查封状况	查封文号	(2024)苏0904执2223号
	查封期限	2024年11月04日起2027年11月03日止
	查封机关	江苏省盐城市大丰区人民法院
查封状况	查封文号	(2024)苏0612执4306号
	查封期限	2024年11月12日起2027年11月11日止
	查封机关	江苏省南通市通州区人民法院
查封状况	查封文号	(2024)浙0521执保5545号
	查封期限	2024年12月12日起2027年12月11日止
	查封机关	德清县人民法院
查封状况	查封文号	(2024)浙1023执2348号
	查封期限	2024年12月17日起2027年12月16日止
	查封机关	天台县人民法院
查封状况	查封文号	(2024)皖1522民初10656号、(2024)皖1522执保2224号
	查封期限	2025年02月08日起2028年02月07日止
	查封机关	安徽省霍邱县人民法院
查封状况	查封文号	(2025)浙0110执7369号
	查封期限	2025年08月11日起2028年08月10日止
	查封机关	杭州市余杭区人民法院
查封状况	查封文号	(2025)浙0521执保3061号
	查封期限	2025年08月22日起2028年08月21日止
	查封机关	德清县人民法院
查封状况	查封文号	(2025)浙0203执7726号
	查封期限	2025年11月17日起2028年11月16日止
	查封机关	宁波市海曙区人民法院
居住权状况	无	
地役权状况	无	
异议状况	无	

该记录依申请用于 **法院委托评估**。



说明:

- 1、本查询记录范围为办理过登记的不动产登记信息(不含预售合同各案信息)，涵盖杭州市上城区、拱墅区、西湖区、钱塘区、滨江区、萧山区、余杭区、临平区、富阳区、临安区和淳安县、桐庐县、建德市。(余1)
- 2、本查询记录涉及到萧山区、余杭区、临平区、富阳区、临安区、淳安县、桐庐县、建德市属地不动产查封的，请至属地进一步核实不动产信息。
- 3、申请人请当场核实以上身份信息 and 结果信息，如信息有误请及时告知工作人员，如隐瞒不报或提供虚假信息的，需自行承担法律责任。
- 4、申请人对以上查询中涉及国家秘密、个人隐私和商业秘密的信息负有保密义务，不得泄露给他人，也不得不正当使用。

杭州市不动产登记信息查询记录

编号：2025-YHSMZJwangsm-021113

依 杭州市余杭区人民法院 申请查询坐落于 仁和街道仁和印象4幢2单元903室 的不动产登记信息，经查询杭州市不动产登记信息管理系统，结果如下：

不动产坐落		仁和街道仁和印象4幢2单元903室					
用途	住宅	建筑面积 (m²)	--	土地使用权 面积 (m²)	44.9	使用期限	2006年01月18日至 2076年01月17日
限制信息	土地:有查封,有抵押					宗地号	330110109001GB03046
不动产状况	权利人						
	权证号 (证明号)	杭余商国用(2012)第09388号					
	权利类型	国有建设用地使用权	权利性质		出让		
	共有情况	--	登记日期		2012年07月17日		
	权利状态	现状					
	附记	--					
抵押状况	抵押权人	浙商银行股份有限公司杭州分行		登记证明号		浙(2021)杭州市不动产证明第2086878号	
	抵押方式	最高额抵押		债权数额		217.8万元	
	登记日期	2021年12月23日		债务履行期限 (债权确定期间)		2021年12月14日起2031年12月14日止	
	附记	存在禁止或限制转让抵押不动产的约定债务人:					
查封状况	查封文号	(2024)浙0281执902号					
	查封期限	2024年03月26日起2027年03月25日止					
	查封机关	余姚市人民法院					
查封状况	查封文号	(2024)浙0521民诉前调3926号					
	查封期限	2024年05月21日起2027年05月20日止					
	查封机关	浙江省德清县人民法院					
查封状况	查封文号	(2024)苏0904民初2986号					
	查封期限	2024年05月27日起2027年05月26日止					
	查封机关	江苏省盐城市大丰区人民法院					
查封状况	查封文号	(2024)苏0682执2549号					
	查封期限	2024年06月03日起2027年06月02日止					
	查封机关	江苏省如皋市人民法院					
查封状况	查封文号	(2024)浙0521执保1706号					
	查封期限	2024年06月24日起2027年06月23日止					
	查封机关	德清县人民法院					

查封状况	查封文号	(2024)苏0904执2223号
	查封期限	2024年11月04日起2027年11月03日止
	查封机关	江苏省盐城市大丰区人民法院
查封状况	查封文号	(2024)苏0612执4306号
	查封期限	2024年11月12日起2027年11月11日止
	查封机关	江苏省南通市通州区人民法院
查封状况	查封文号	(2024)浙0521执保5545号
	查封期限	2024年12月12日起2027年12月11日止
	查封机关	德清县人民法院
查封状况	查封文号	(2024)浙1023执2348号
	查封期限	2024年12月17日起2027年12月16日止
	查封机关	天台县人民法院
查封状况	查封文号	(2024)皖1522民初10656号、(2024)皖1522执保2224号
	查封期限	2025年02月08日起2028年02月07日止
	查封机关	安徽省霍邱县人民法院
查封状况	查封文号	(2025)浙0110执7369号
	查封期限	2025年08月11日起2028年08月10日止
	查封机关	杭州市余杭区人民法院
查封状况	查封文号	(2025)浙0521执保3061号
	查封期限	2025年08月22日起2028年08月21日止
	查封机关	德清县人民法院
查封状况	查封文号	(2025)浙0203执7726号
	查封期限	2025年11月17日起2028年11月16日止
	查封机关	宁波市海曙区人民法院
居住权状况	无	
地役权状况	无	
异议状况	无	

该记录依申请用于 法院委托评估 。




说明：
1、本查询记录范围为办理过登记的不动产登记信息(不含预售合同备案信息)，涵盖杭州市上城区、拱墅区、西湖区、钱塘区、滨江区、萧山区、余杭区、临平区、富阳区、临安区和淳安县、桐庐县、建德市。
2、本查询记录涉及到萧山区、余杭区、临平区、富阳区、临安区、淳安县、桐庐县、建德市属地不动产查封的，请至属地进一步核实不动产信息。
3、申请人请当场核实以上身份信息和结果信息，如信息有误请及时告知工作人员，如隐瞒不报或提供虚假信息的，需自行承担法律责任。
4、申请人对以上查询中涉及国家秘密、个人隐私和商业秘密的信息负有保密义务，不得泄露给他人，也不得不正当使用。

房产分层分户平面图

图幅号:

房屋座落	杭州市余杭区仁和镇仁和印象4幢2单元903室			地号	
建成年份	2008	所在层次	9	套内面积(m ²)	87.11
设计用途	住宅	地上总层数	13	分摊面积(m ²)	17.98
建筑结构	钢筋混凝土	地下总层数	0	建筑面积(m ²)	105.09

53132008

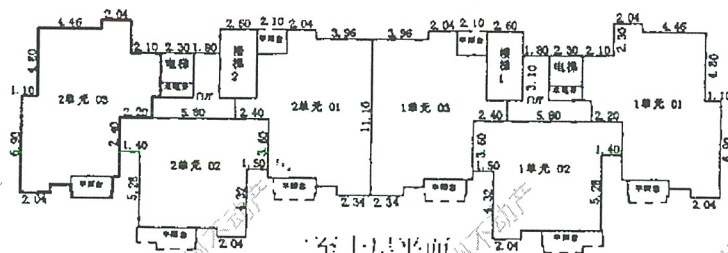

至1.5层平面

杭州余杭同创测绘有限公司

比例尺

1:500

102.0-73.0

密级

73.20

73.30

73.40

73.43

02.57

02.57

02.50

02.50

02.40

02.40

02.30

02.30

02.24

02.24


73.18

73.20

73.30

73.40

73.43

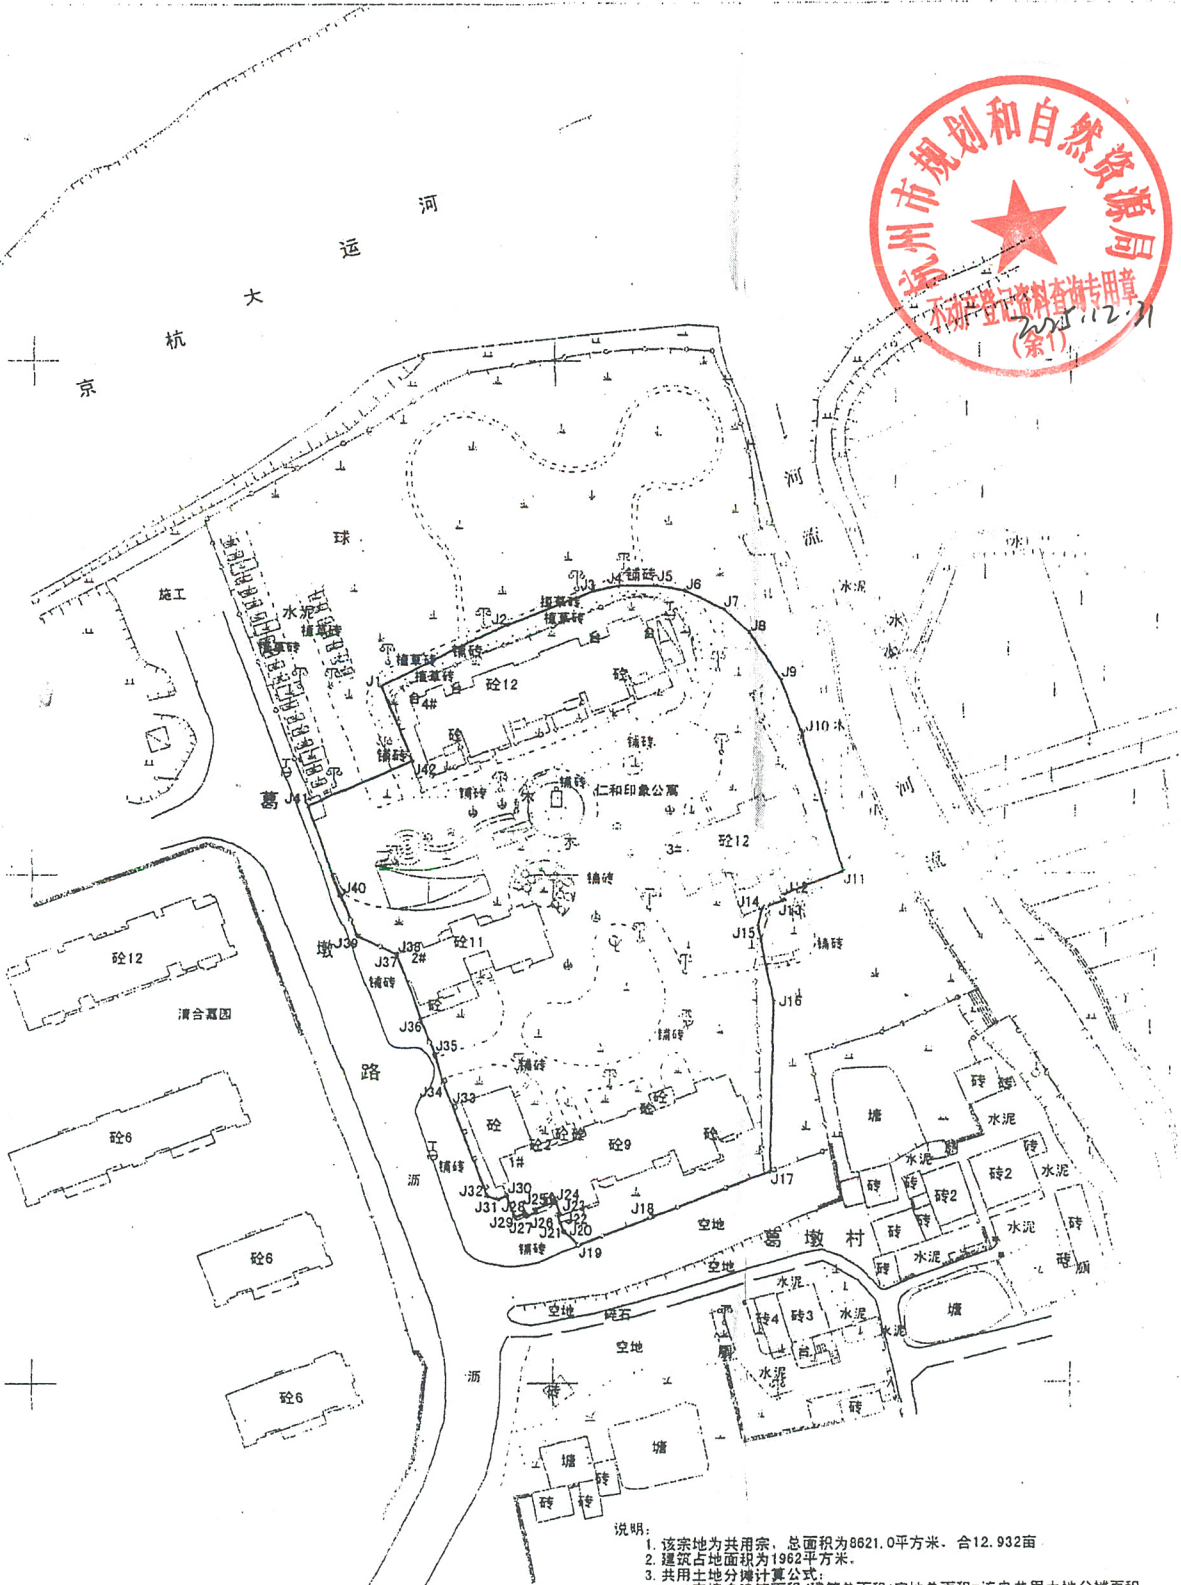

说明:

1. 该宗地为共用宗, 总面积为8621.0平方米, 合12.932亩
2. 建筑占地面积为1962平方米
3. 共用土地分摊计算公式:
$$\text{申请户建筑面积} \cdot \text{建筑总面积} \div \text{宗地总面积} = \text{该户共用土地分摊面积}$$